+157
+158.5
+161
+162
+166.5
+167
+168
+181

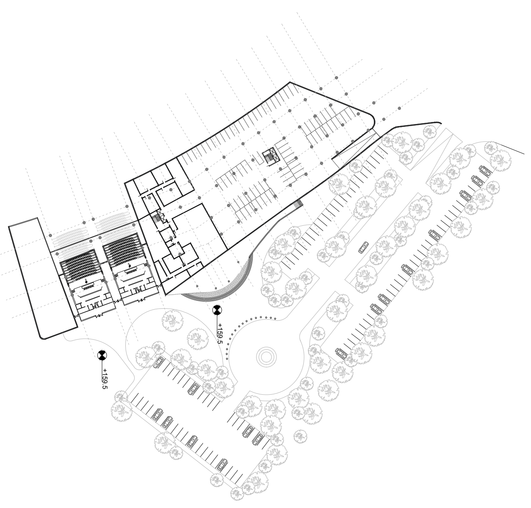
UNO
UNO
+159.5
+159.5

+157
+158.5
+161
+156
+160
+159
+157
+162
+158
+158.5
+161
+162
+158.5
+157

+157
+160
+157
+160.5
+158
+162
+157
+161
+158.5
+158
+160
+156
+161
+158.5
+157

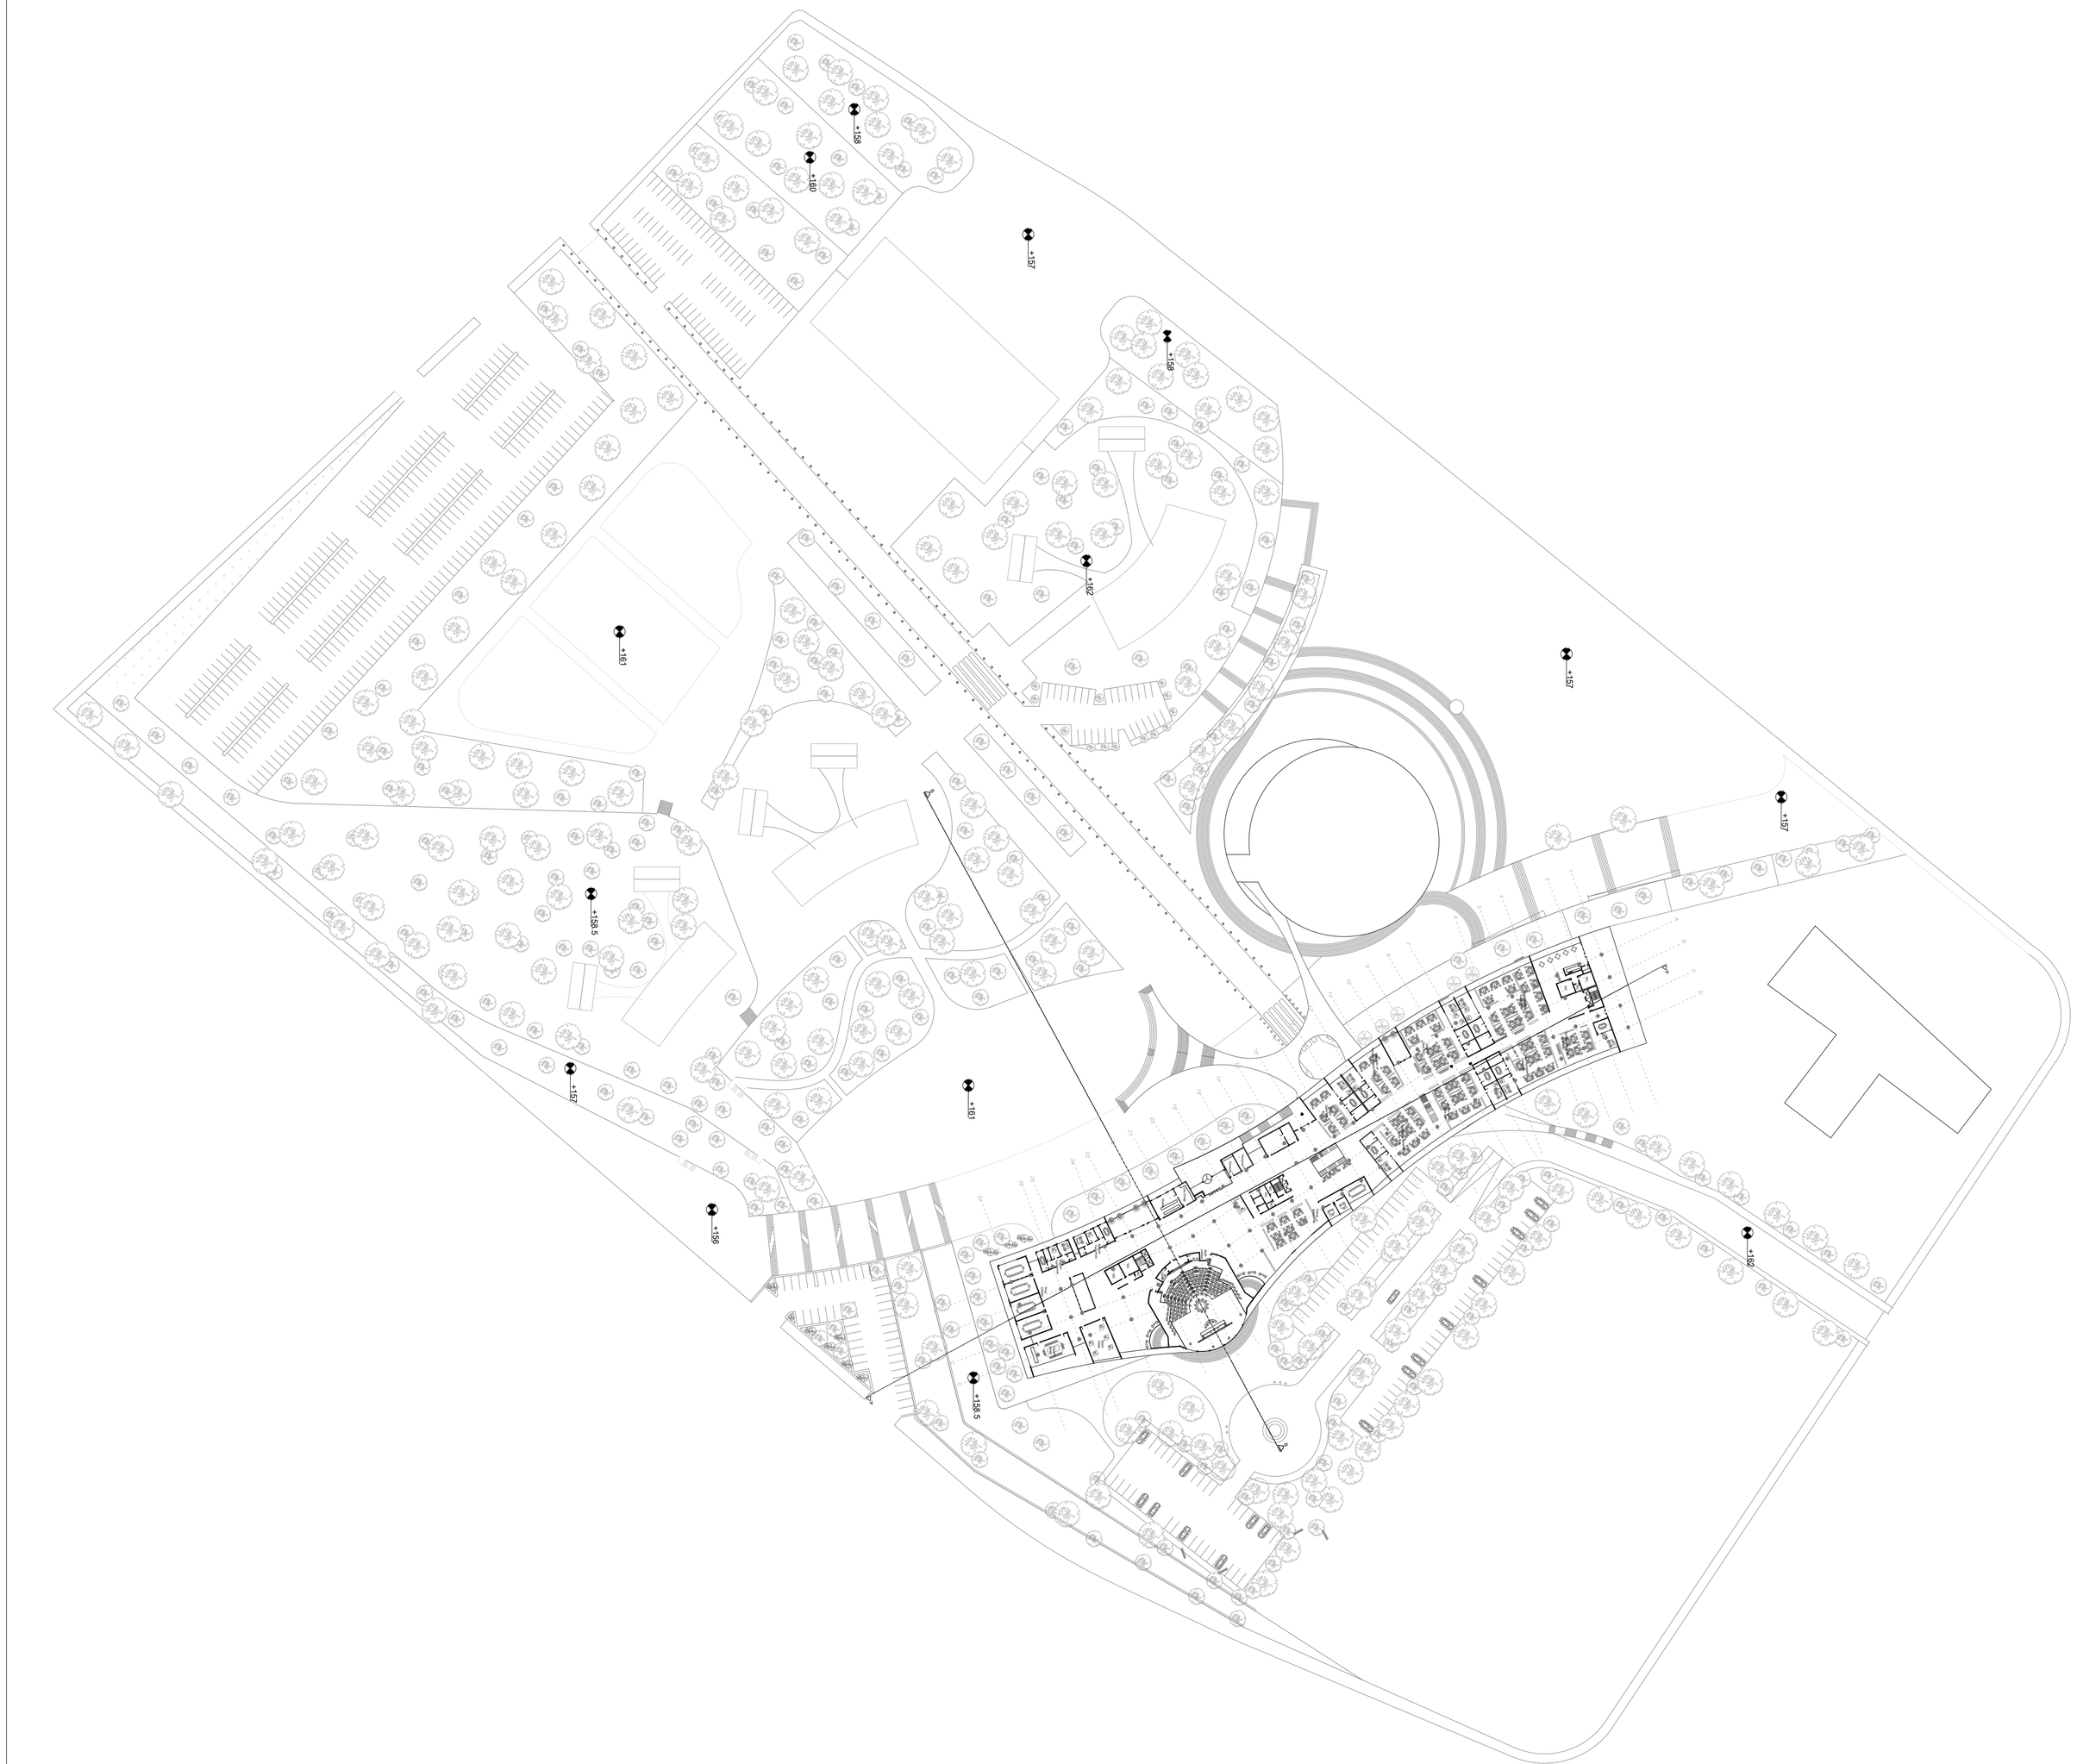
+158
+160
+157
+159
+162
+161
+157
+158.5
+157
+161
+157
+156
+160
+160.5

+158
+160
+157
+159
+162
+161
+157
+157
+158.5
+157
+161
+159
+162
+158.5

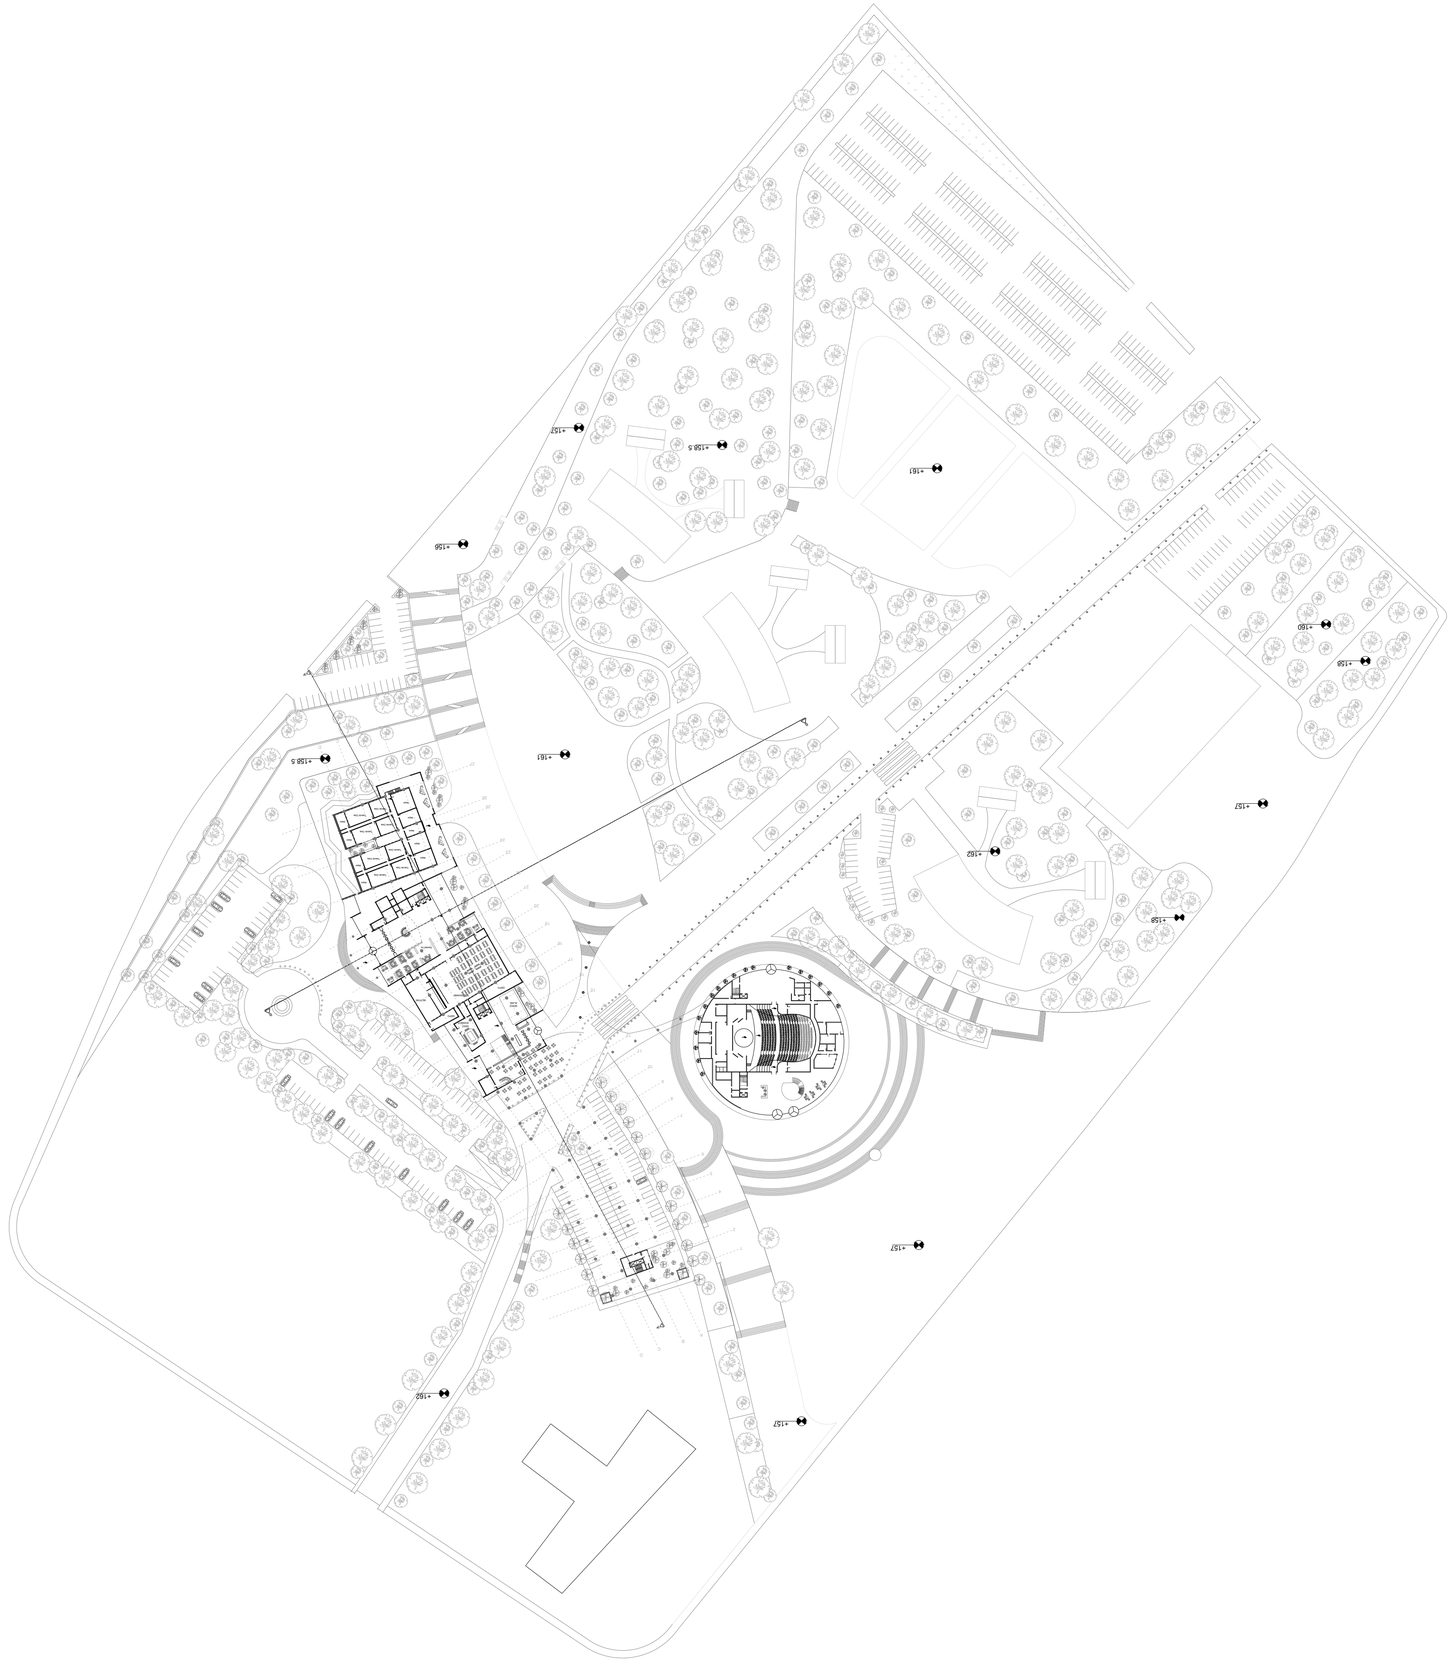
+156
+157
+158.5
+161
+162
+160
+159
+157
+162
+158
+157
+161
+158.5
+162
+157

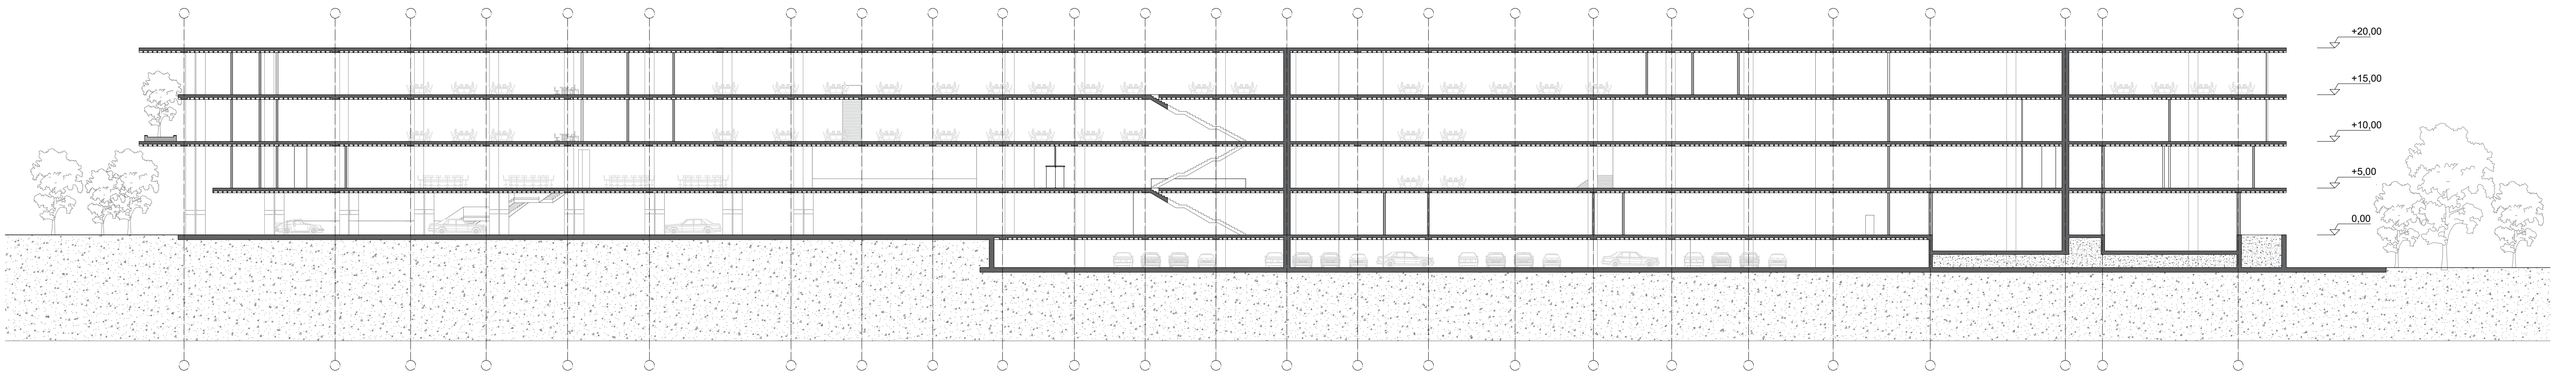

A-A KESİTİ

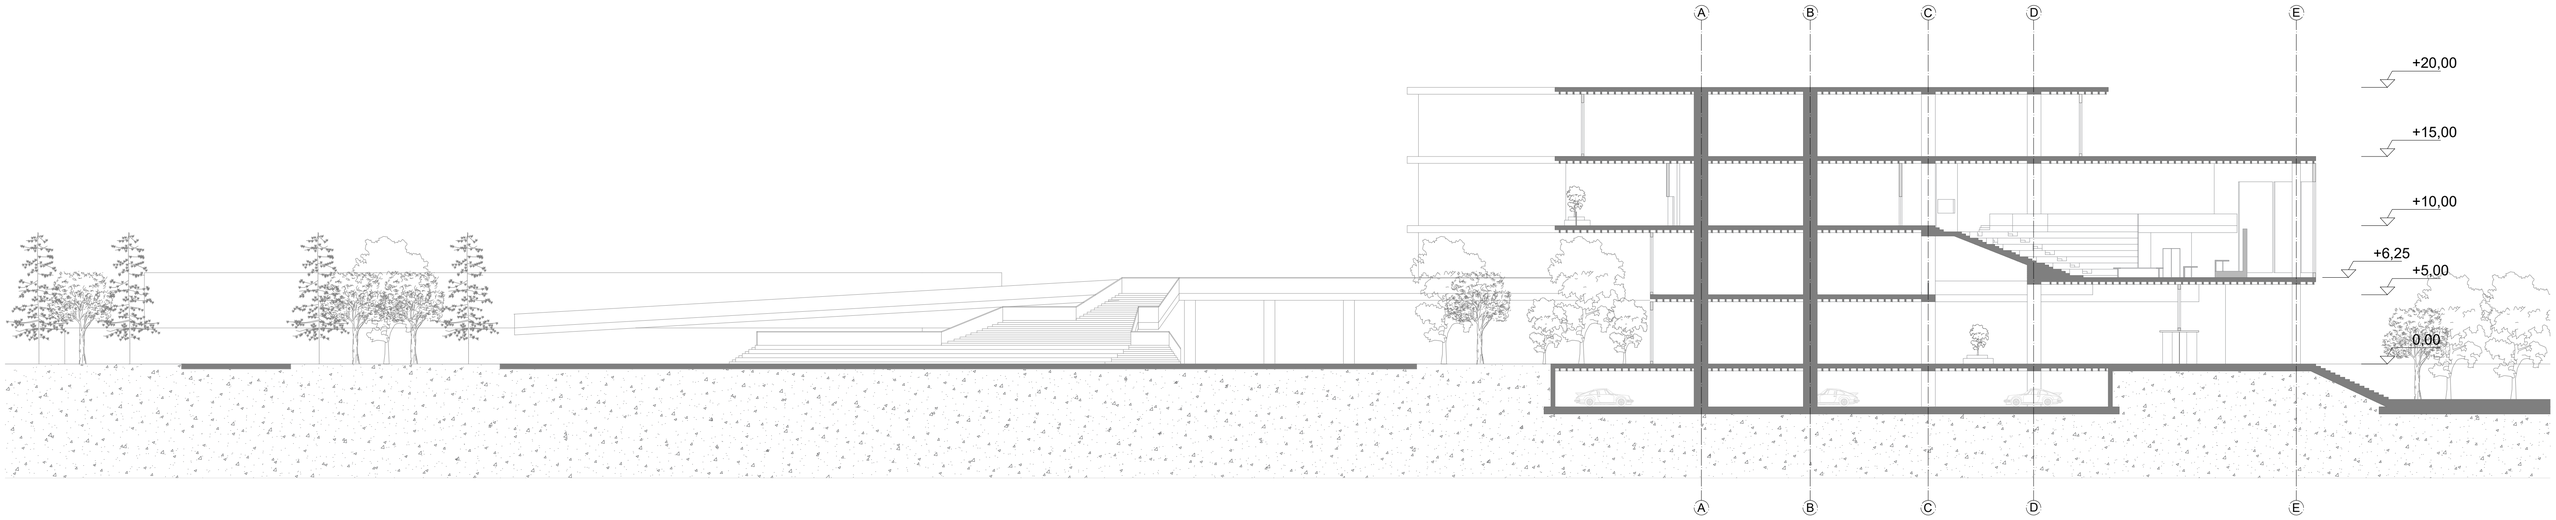

B-B KESİTİ

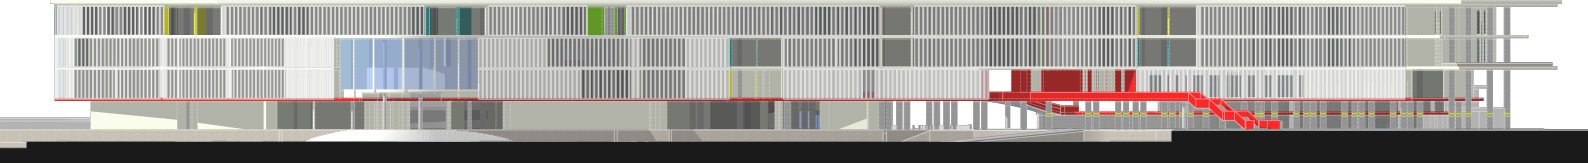

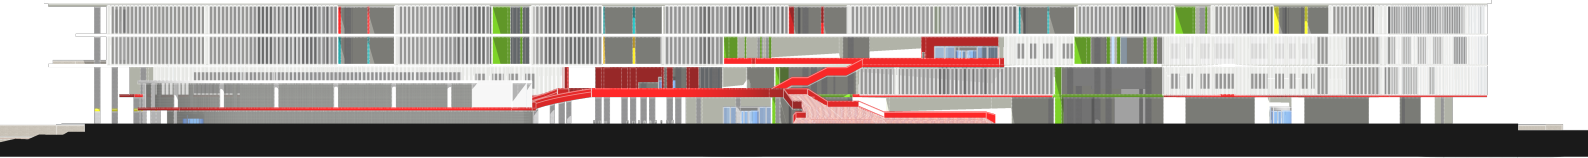

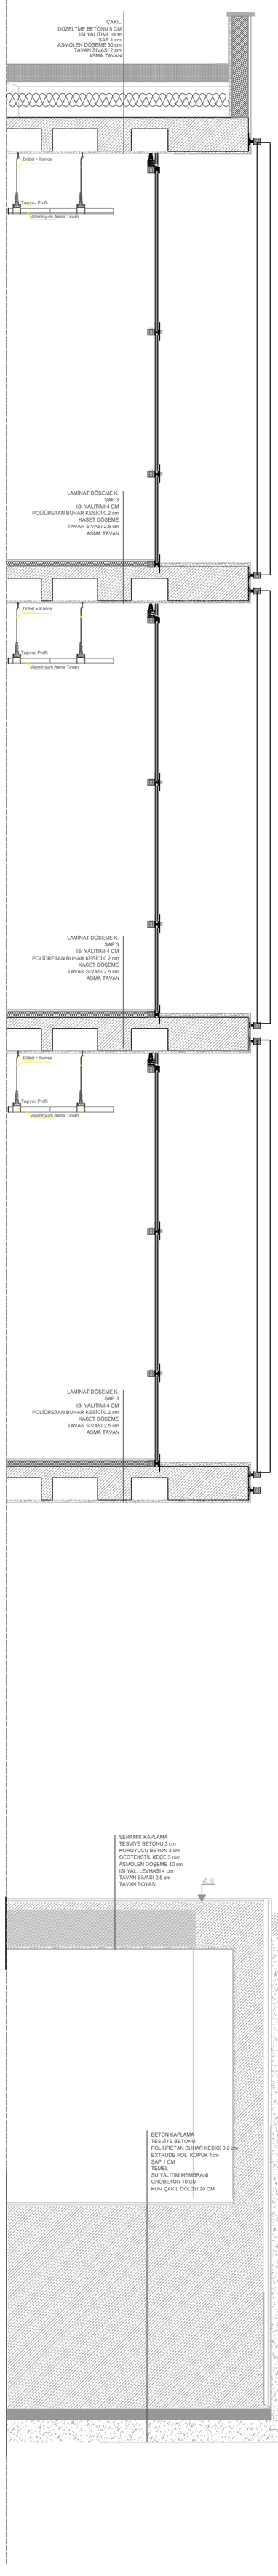
ÇAKİL
DÜZELTME BETONU 5 CM
ISI YALITIMI 10cm
ŞAP 1 cm
ASMOLEN DÖŞEME 30 cm
TAVAN SIVASI 2 cm
ASMA TAVAN
Dübel + Kanca
Taşıyıcı Profil
Alüminyum Asma Tavan
LAMİNAT DÖŞEME K.
ŞAP 3
ISI YALITIMI 4 CM
POLİÜRETAN BUHAR KESİCİ 0.2 cm
KASET DÖŞEME
TAVAN SIVASI 2.5 cm
ASMA TAVAN
Dübel + Kanca
Taşıyıcı Profil
Alüminyum Asma Tavan
LAMİNAT DÖŞEME K.
ŞAP 3
ISI YALITIMI 4 CM
POLİÜRETAN BUHAR KESİCİ 0.2 cm
KASET DÖŞEME
TAVAN SIVASI 2.5 cm
ASMA TAVAN
Dübel + Kanca
Taşıyıcı Profil
Alüminyum Asma Tavan
LAMİNAT DÖŞEME K.
ŞAP 3
ISI YALITIMI 4 CM
POLİÜRETAN BUHAR KESİCİ 0.2 cm
KASET DÖŞEME
TAVAN SIVASI 2.5 cm
ASMA TAVAN
SERAMİK KAPLAMA
TESVİYE BETONU 3 cm
KORUYUCU BETON 3 cm
GEOTEKSTİL KEÇE 3 mm
ASMOLEN DÖŞEME 40 cm
ISI YAL. LEVHASI 4 cm
TAVAN SIVASI 2.5 cm
TAVAN BOYASI
+0.10
TARAKLI MOZAİK KAPLAMA
TESVİYE BETONU
GROBETON 10cm
TUVENAN DOLGU
±0.00
BETON KAPLAMA
TESVİYE BETONU
POLİÜRETAN BUHAR KESİCİ 0.2 cm
EXTRUDE POL. KÖPÜK 1cm
ŞAP 1 CM
TEMEL
SU YALITIM MEMBRANI
GROBETON 10 CM
KUM ÇAKIL DOLGU 20 CM